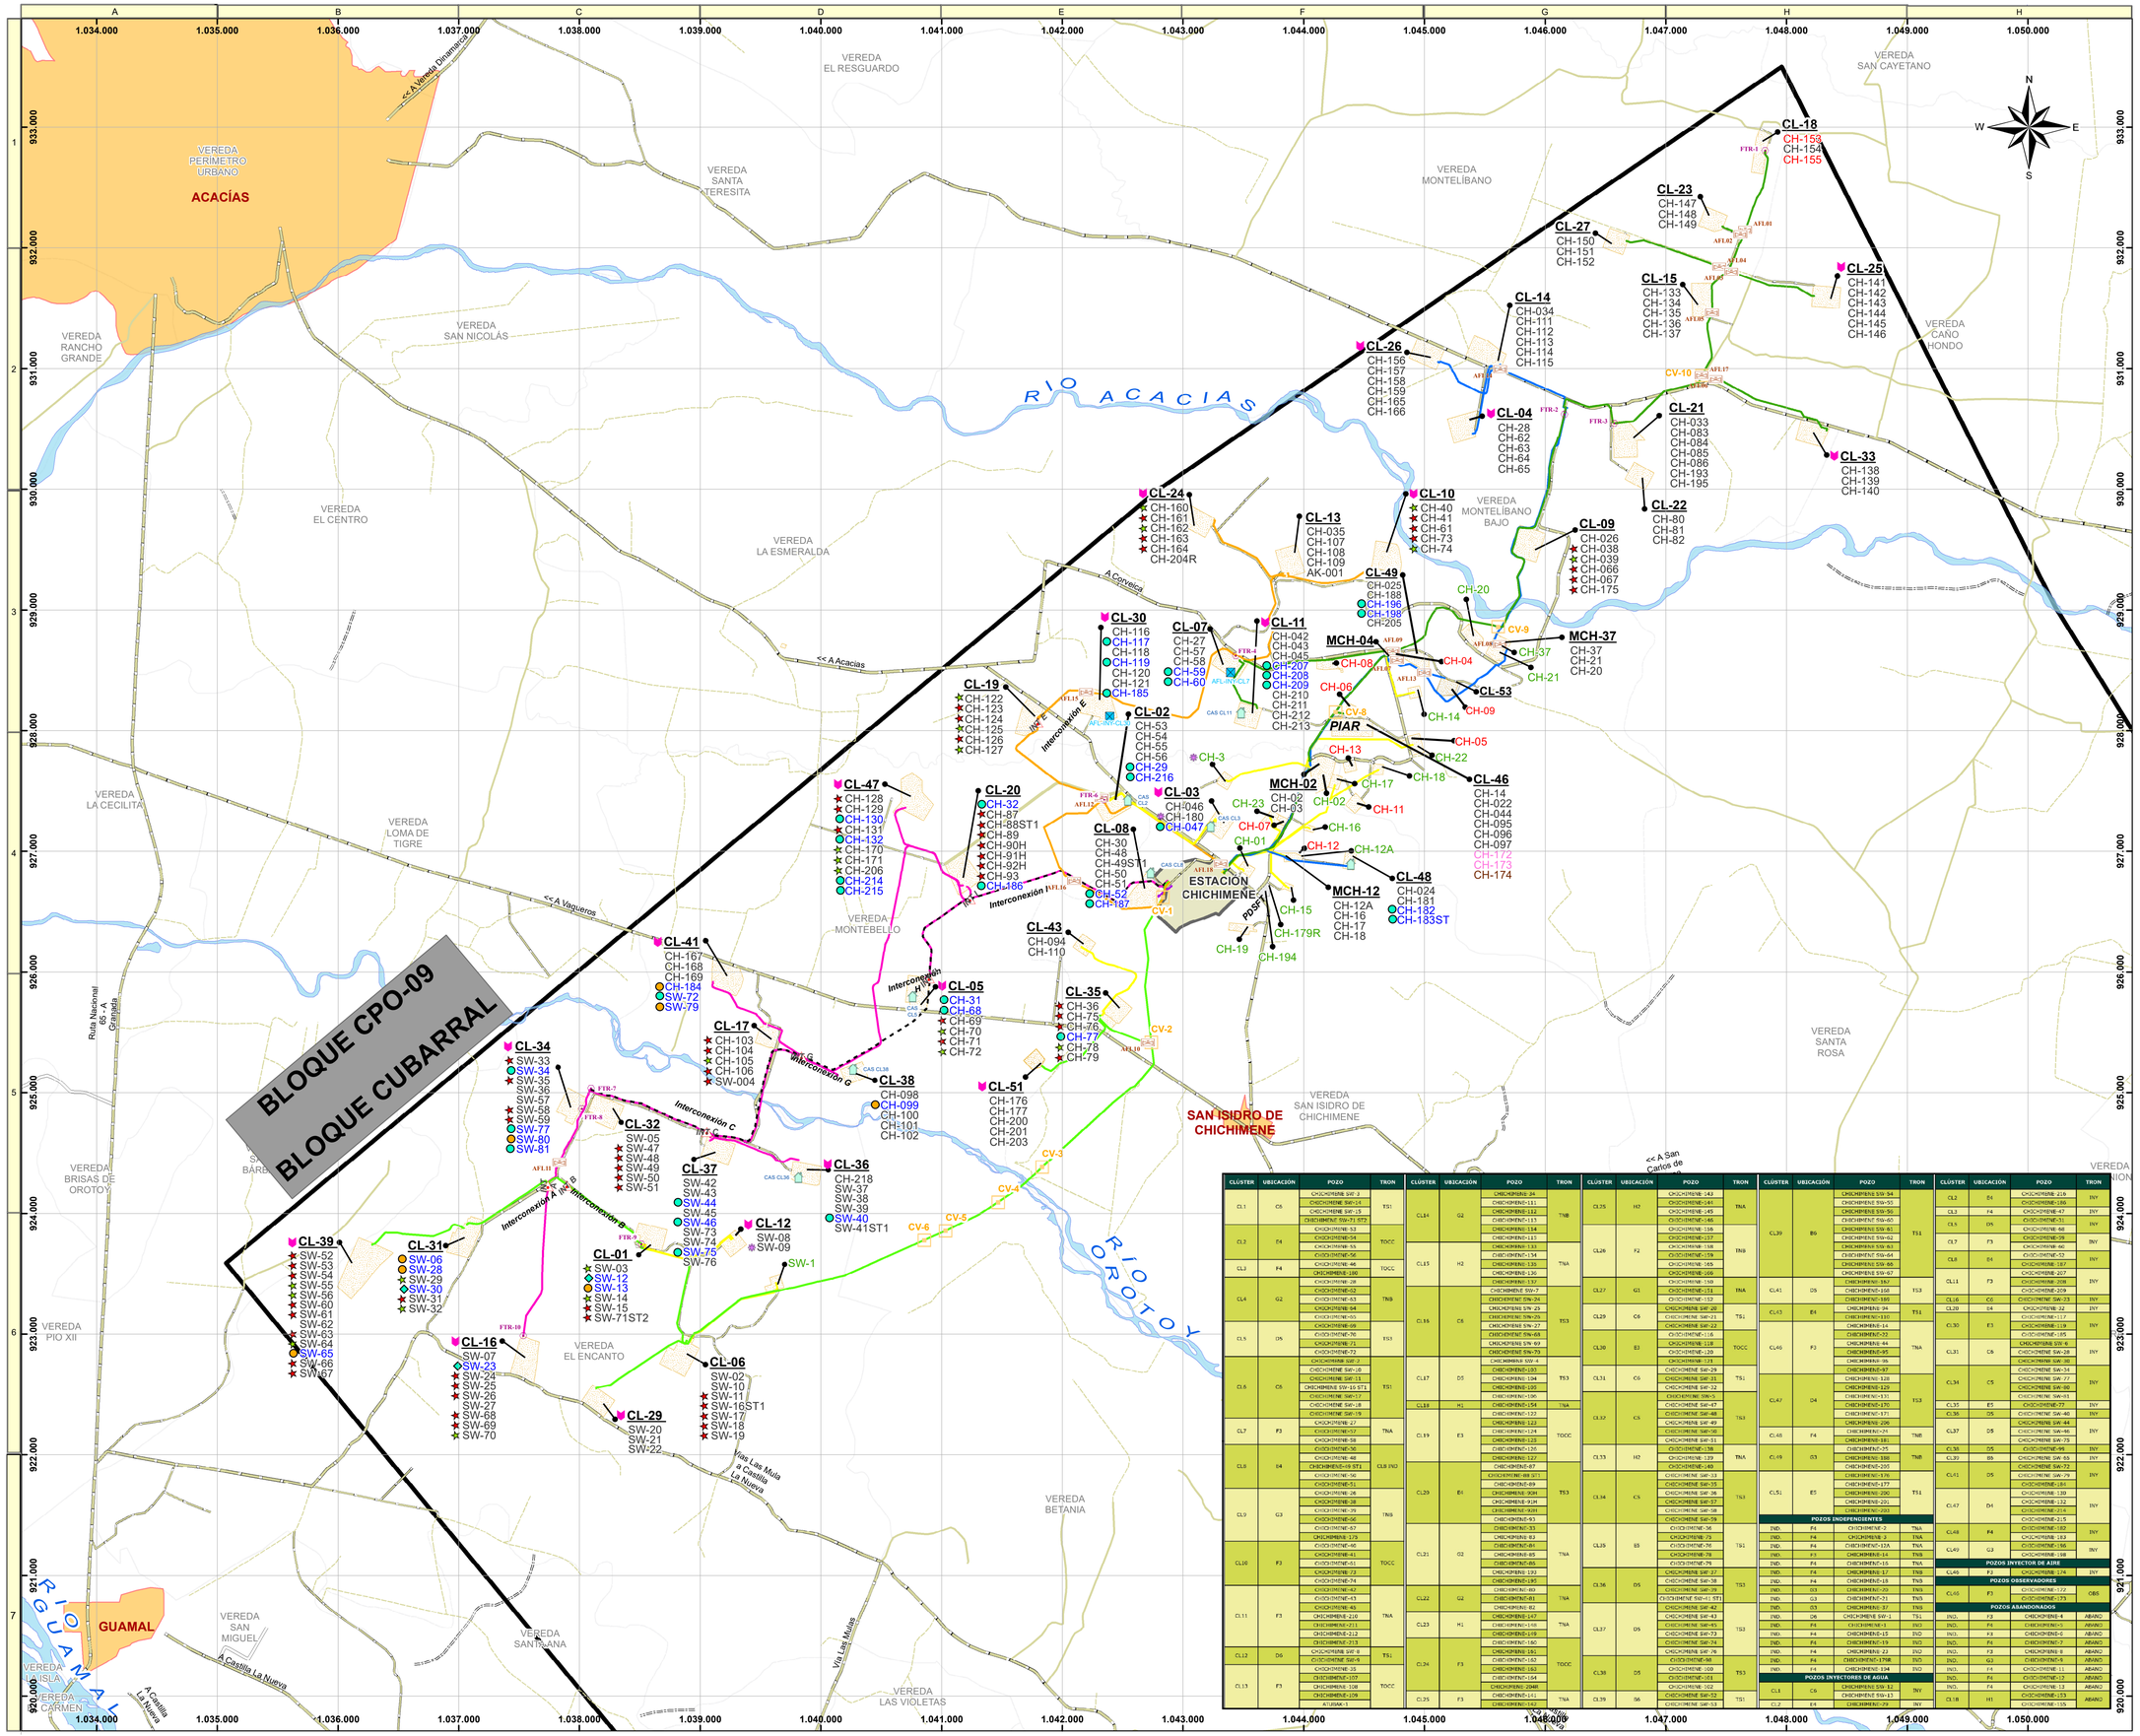

CLÚSTER	UBICACIÓN	POZO	TRON
CL1	C6	CHICHIMENE SW-3	TS1
		CHICHIMENE SW-14	
		CHICHIMENE SW-15	
		CHICHIMENE SW-71 ST2	
CL2	E4	CHICHIMENE-53	TOCC
		CHICHIMENE-54	
		CHICHIMENE-55	
		CHICHIMENE-56	
CL3	F4	CHICHIMENE-46	TOCC
		CHICHIMENE-166	
CL4	G2	CHICHIMENE-28	TNB
		CHICHIMENE-62	
		CHICHIMENE-63	
		CHICHIMENE-64	
CL5	D5	CHICHIMENE-65	TS3
		CHICHIMENE-70	
		CHICHIMENE-71	
		CHICHIMENE-72	
CL6	C6	CHICHIMENE SW-2	TS1
		CHICHIMENE SW-10	
		CHICHIMENE SW-11	
		CHICHIMENE SW-19 ST1	
		CHICHIMENE SW-17	
		CHICHIMENE SW-28	
		CHICHIMENE SW-19	
CL7	F3	CHICHIMENE-27	TNA
		CHICHIMENE-57	
		CHICHIMENE-58	
		CHICHIMENE-59	
CL8	E4	CHICHIMENE-60	TNA
		CHICHIMENE-48	
		CHICHIMENE-49 ST1	
		CHICHIMENE-50	CL8 IND
CL9	G3	CHICHIMENE-1	TNB
		CHICHIMENE-26	
		CHICHIMENE-38	
		CHICHIMENE-39	
		CHICHIMENE-40	
CL10	F3	CHICHIMENE-67	TOCC
		CHICHIMENE-175	
		CHICHIMENE-45	
		CHICHIMENE-41	
		CHICHIMENE-42	
		CHICHIMENE-72	
		CHICHIMENE-74	
CL11	F3	CHICHIMENE-42	TNA
		CHICHIMENE-43	
		CHICHIMENE-211	
		CHICHIMENE-212	
		CHICHIMENE-213	
CL12	D6	CHICHIMENE SW-8	TS1
		CHICHIMENE SW-9	
CL13	F3	CHICHIMENE-35	TOCC
		CHICHIMENE-107	
		CHICHIMENE-108	
		CHICHIMENE-109	
		AIURAK-1	
CL14	G2	CHICHIMENE-24	TNB
		CHICHIMENE-11	
		CHICHIMENE-112	
		CHICHIMENE-113	
		CHICHIMENE-114	
CL15	H2	CHICHIMENE-115	TNA
		CHICHIMENE-132	
		CHICHIMENE-133	
		CHICHIMENE-134	
		CHICHIMENE-135	
		CHICHIMENE-136	
CL16	C6	CHICHIMENE-137	TS3
		CHICHIMENE SW-7	
		CHICHIMENE SW-24	
		CHICHIMENE SW-25	
		CHICHIMENE SW-26	
		CHICHIMENE SW-27	
		CHICHIMENE SW-68	
		CHICHIMENE SW-69	
		CHICHIMENE SW-70	
CL17	D5	CHICHIMENE SW-4	TS3
		CHICHIMENE-103	
		CHICHIMENE-104	
		CHICHIMENE-105	
		CHICHIMENE-106	
CL18	H1	CHICHIMENE-154	TNA
CL19	E3	CHICHIMENE-122	TOCC
		CHICHIMENE-123	
		CHICHIMENE-124	
		CHICHIMENE-125	
		CHICHIMENE-126	
		CHICHIMENE-127	
		CHICHIMENE-67	
CL20	E6	CHICHIMENE-88 ST1	TS3
		CHICHIMENE-89	
		CHICHIMENE-90H	
		CHICHIMENE-91H	
		CHICHIMENE-92H	
		CHICHIMENE-93	
CL21	G2	CHICHIMENE-33	TNA
		CHICHIMENE-83	
		CHICHIMENE-84	
		CHICHIMENE-85	
		CHICHIMENE-86	
		CHICHIMENE-193	
		CHICHIMENE-195	
		CHICHIMENE-40	
CL22	G2	CHICHIMENE-81	TNA
		CHICHIMENE-82	
CL23	H1	CHICHIMENE-147	TNA
		CHICHIMENE-148	
		CHICHIMENE-149	
		CHICHIMENE-150	
		CHICHIMENE-162	
CL24	F3	CHICHIMENE-163	TOCC
		CHICHIMENE-164	
		CHICHIMENE-204R	
CL25	F3	CHICHIMENE-204M	TNA
		CHICHIMENE-143	
CL25	H2	CHICHIMENE-144	TNA
		CHICHIMENE-145	
		CHICHIMENE-146	
		CHICHIMENE-156	
		CHICHIMENE-157	
CL26	F2	CHICHIMENE-158	TNB
		CHICHIMENE-159	
		CHICHIMENE-165	
		CHICHIMENE-166	
		CHICHIMENE-160	
CL27	G1	CHICHIMENE-151	TNA
		CHICHIMENE-152	
CL29	C6	CHICHIMENE SW-20	TS1
		CHICHIMENE SW-21	
CL30	B3	CHICHIMENE-116	TOCC
		CHICHIMENE-128	
		CHICHIMENE-129	
		CHICHIMENE-173	
CL31	C6	CHICHIMENE SW-29	TS1
		CHICHIMENE SW-31	
		CHICHIMENE SW-32	
		CHICHIMENE SW-33	
CL32	C5	CHICHIMENE SW-47	TS3
		CHICHIMENE SW-48	
		CHICHIMENE SW-49	
		CHICHIMENE SW-50	
		CHICHIMENE SW-51	
		CHICHIMENE-136	
CL33	H2	CHICHIMENE-139	TNA
		CHICHIMENE-140	
		CHICHIMENE SW-33	
CL34	C5	CHICHIMENE SW-35	TS3
		CHICHIMENE SW-36	
		CHICHIMENE SW-37	
		CHICHIMENE SW-38	
		CHICHIMENE SW-59	
		CHICHIMENE SW-75	
		CHICHIMENE-36	
CL35	B5	CHICHIMENE-73	TS1
		CHICHIMENE-76	
		CHICHIMENE-78	
		CHICHIMENE-79	
		CHICHIMENE-15	
CL36	D5	CHICHIMENE SW-27	TS3
		CHICHIMENE SW-38	
		CHICHIMENE SW-39	
		CHICHIMENE SW-41 ST1	
		CHICHIMENE SW-42	
CL37	D5	CHICHIMENE SW-43	TS3
		CHICHIMENE SW-45	
		CHICHIMENE SW-73	
		CHICHIMENE SW-74	
		CHICHIMENE SW-76	
CL38	D5	CHICHIMENE-98	TS3
		CHICHIMENE-100	
		CHICHIMENE-101	
		CHICHIMENE-102	
		CHICHIMENE SW-52	
CL39	B6	CHICHIMENE-29	TS1
		CHICHIMENE SW-54	
		CHICHIMENE SW-55	
		CHICHIMENE SW-56	
		CHICHIMENE SW-60	
		CHICHIMENE SW-61	
		CHICHIMENE SW-62	
		CHICHIMENE SW-63	
		CHICHIMENE SW-64	
		CHICHIMENE SW-65	
		CHICHIMENE SW-66	
		CHICHIMENE SW-67	
CL41	D5	CHICHIMENE-167	TS3
		CHICHIMENE-168	
		CHICHIMENE-169	
CL43	E4	CHICHIMENE-94	TS1
		CHICHIMENE-95	
		CHICHIMENE-96	
		CHICHIMENE-97	
CL46	F4	CHICHIMENE-128	TS3
		CHICHIMENE-129	
		CHICHIMENE-131	
		CHICHIMENE-170	
		CHICHIMENE-171	
CL47	D4	CHICHIMENE-256	TS3
		CHICHIMENE-24	
CL48	F4	CHICHIMENE-181	TNB
		CHICHIMENE-55	
CL49	D3	CHICHIMENE-188	TNB
		CHICHIMENE-205	
CL51	E5	CHICHIMENE-178	TS1
		CHICHIMENE-177	
		CHICHIMENE-200	
		CHICHIMENE-201	
		CHICHIMENE-203	
POZOS INDEPENDIENTES			
IND.	F4	CHICHIMENE-2	TNA
IND.	F4	CHICHIMENE-3	TNA
IND.	F4	CHICHIMENE-12A	TNA
IND.	F3	CHICHIMENE-14	TNA
IND.	F4	CHICHIMENE-16	TNA
IND.	F4	CHICHIMENE-17	TNB
IND.	F4	CHICHIMENE-18	TNB
IND.	D3	CHICHIMENE-20	TNB
IND.	G3	CHICHIMENE-71	TNB
IND.	D3	CHICHIMENE-87	TNB
IND.	D6	CHICHIMENE SW-1	TS1
IND.	F4	CHICHIMENE-4	INY
IND.	F4	CHICHIMENE-15	INY
IND.	F4	CHICHIMENE-19	INY
IND.	F4	CHICHIMENE-23	INY
IND.	F4	CHICHIMENE-179R	INY
IND.	F4	CHICHIMENE-194	INY
POZOS INYECTORES DE AGUA			
CL8	C6	CHICHIMENE SW-12	INY
		CHICHIMENE SW-13	
CL2	E4	CHICHIMENE-29	INY
CL2	E4	CHICHIMENE-216	INY
CL3	F4	CHICHIMENE-30	INY
CL4	F4	CHICHIMENE-47	INY
CL5	D5	CHICHIMENE-51	INY
		CHICHIMENE-68	
CL7	F3	CHICHIMENE-78	INY
		CHICHIMENE-96	
CL8	E4	CHICHIMENE-52	INY
		CHICHIMENE-187	
		CHICHIMENE-207	
CL11	F3	CHICHIMENE-208	INY
		CHICHIMENE-209	
CL16	C6	CHICHIMENE SW-33	INY
CL20	E4	CHICHIMENE-32	INY
		CHICHIMENE-117	
CL30	E3	CHICHIMENE-119	INY
		CHICHIMENE-185	
CL31	C6	CHICHIMENE SW-6	INY
		CHICHIMENE SW-28	
		CHICHIMENE SW-30	
CL34	C5	CHICHIMENE SW-34	INY
		CHICHIMENE SW-77	
		CHICHIMENE SW-80	
		CHICHIMENE SW-81	
CL35	E5	CHICHIMENE-77	INY
CL36	D5	CHICHIMENE SW-40	INY
CL37	D5	CHICHIMENE SW-44	INY
		CHICHIMENE SW-46	
		CHICHIMENE SW-75	
CL38	D5	CHICHIMENE-46	INY
CL39	B5	CHICHIMENE SW-55	INY
		CHICHIMENE SW-72	
CL41	D5	CHICHIMENE SW-79	INY
		CHICHIMENE-184	
CL47	D4	CHICHIMENE-130	INY
		CHICHIMENE-132	
		CHICHIMENE-214	
		CHICHIMENE-215	
CL48	F4	CHICHIMENE-182	INY
		CHICHIMENE-183	
CL49	G2	CHICHIMENE-186	INY
		CHICHIMENE-198	
POZOS INYECTOR DE AIRE			
CL46	F2	CHICHIMENE-174	INY
POZOS OBSERVADORES			
CL16	F3	CHICHIMENE-172	OBS
		CHICHIMENE-173	
POZOS ABANDONADOS			
IND.	F3	CHICHIMENE-4	ABANO
IND.	F4	CHICHIMENE-5	ABANO
IND.	F3	CHICHIMENE-6	ABANO
IND.	F4	CHICHIMENE-7	ABANO
IND.	F3	CHICHIMENE-8	ABANO
IND.	G2	CHICHIMENE-9	ABANO
IND.	F4	CHICHIMENE-11	ABANO
IND.	F4	CHICHIMENE-13	ABANO
IND.	F4	CHICHIMENE-14	ABANO
CL1B	H1	CHICHIMENE-153	ABANO
		CHICHIMENE-155	

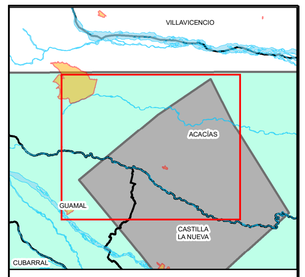

LOCALIZACIÓN

- FACILIDAD DE TRAMPAS
- AFLORAMIENTO VALVULADO
- AFLORAMIENTO VALV INY AGUA
- CASETA INY AGUA
- INTERCONEXIONES
- Troncal Norte A (TNA)
- Troncal Norte B (TNB)
- Troncal Occidental (TOCC)
- Troncal Independiente CL8 (CL8 IND)
- Troncal Sur 1 (TS1)
- Troncal Sur 2 (TS2)
- Troncal Sur 3 (TS3): TS20"-TS16"-TS8"
- Líneas Flujo IND

Via

Tipo

- Vía pavimentada 2 o más carriles
- Vía sin pavimentar 2 o más carriles
- Vía pavimentada angosta
- Vía sin pavimentar angosta
- Camino
- Sendero
- Transitable en tiempo seco
- Caños
- Clúster
- Estación Chichimene
- Rios
- Centro poblado
- Límite vereda

Bloque

- CUBARRAL
- CPO 9

Condición Pozos

- CH-XX Pozo Independiente
- CH-XX Pozo Abandonado
- CH-XX Pozo Productor
- CH-XX Pozo con Dilución en Fondo On
- CH-XX Pozo con Dilución en Fondo Off
- CH-XX Pozo Inyección Convencional Agua Act
- CH-XX Pozo Inyección Convencional Agua Inact
- CH-XX Pozo Inyección Dump Flood Activo
- CH-XX Pozo Inyección Dump Flood Inactivo
- CH-XX Pozo Observador
- CH-XX Pozo Inyección aire
- CH-XX Línea Flujo con Inyección de Nafta
- CL-XX Inyección Nafta Superficie

AREA DE LOCACION — CL-3 — NUMERO DE CLUSTER

CH-46, CH-47 — POZOS DEL CLUSTER

Sistema de Coordenadas: MAGNA Colombia Bogotá
Proyección: Transversal de Mercator
Falso Este: 1000000
Falso Norte: 1000000
Meridiano Central: -74,0775079°
Factor de Escala: 1,000
Latitud de Origen: 4,5962°
Unidades: Metros

ecopetrol — TICE TECNA INTEGRITY AND CORROSION ENGINEERING

LÍNEAS TRONCALES CAMPO CHICHIMENE

Elaboró:
César Muñoz Castellanos
Modificó:
Deisy Liliana Pérez
Revisó:
Yudy Palma Pacheco

Agosto de 2020

1:25.000

0 250 500 1.000 1.500 2.000 Metros